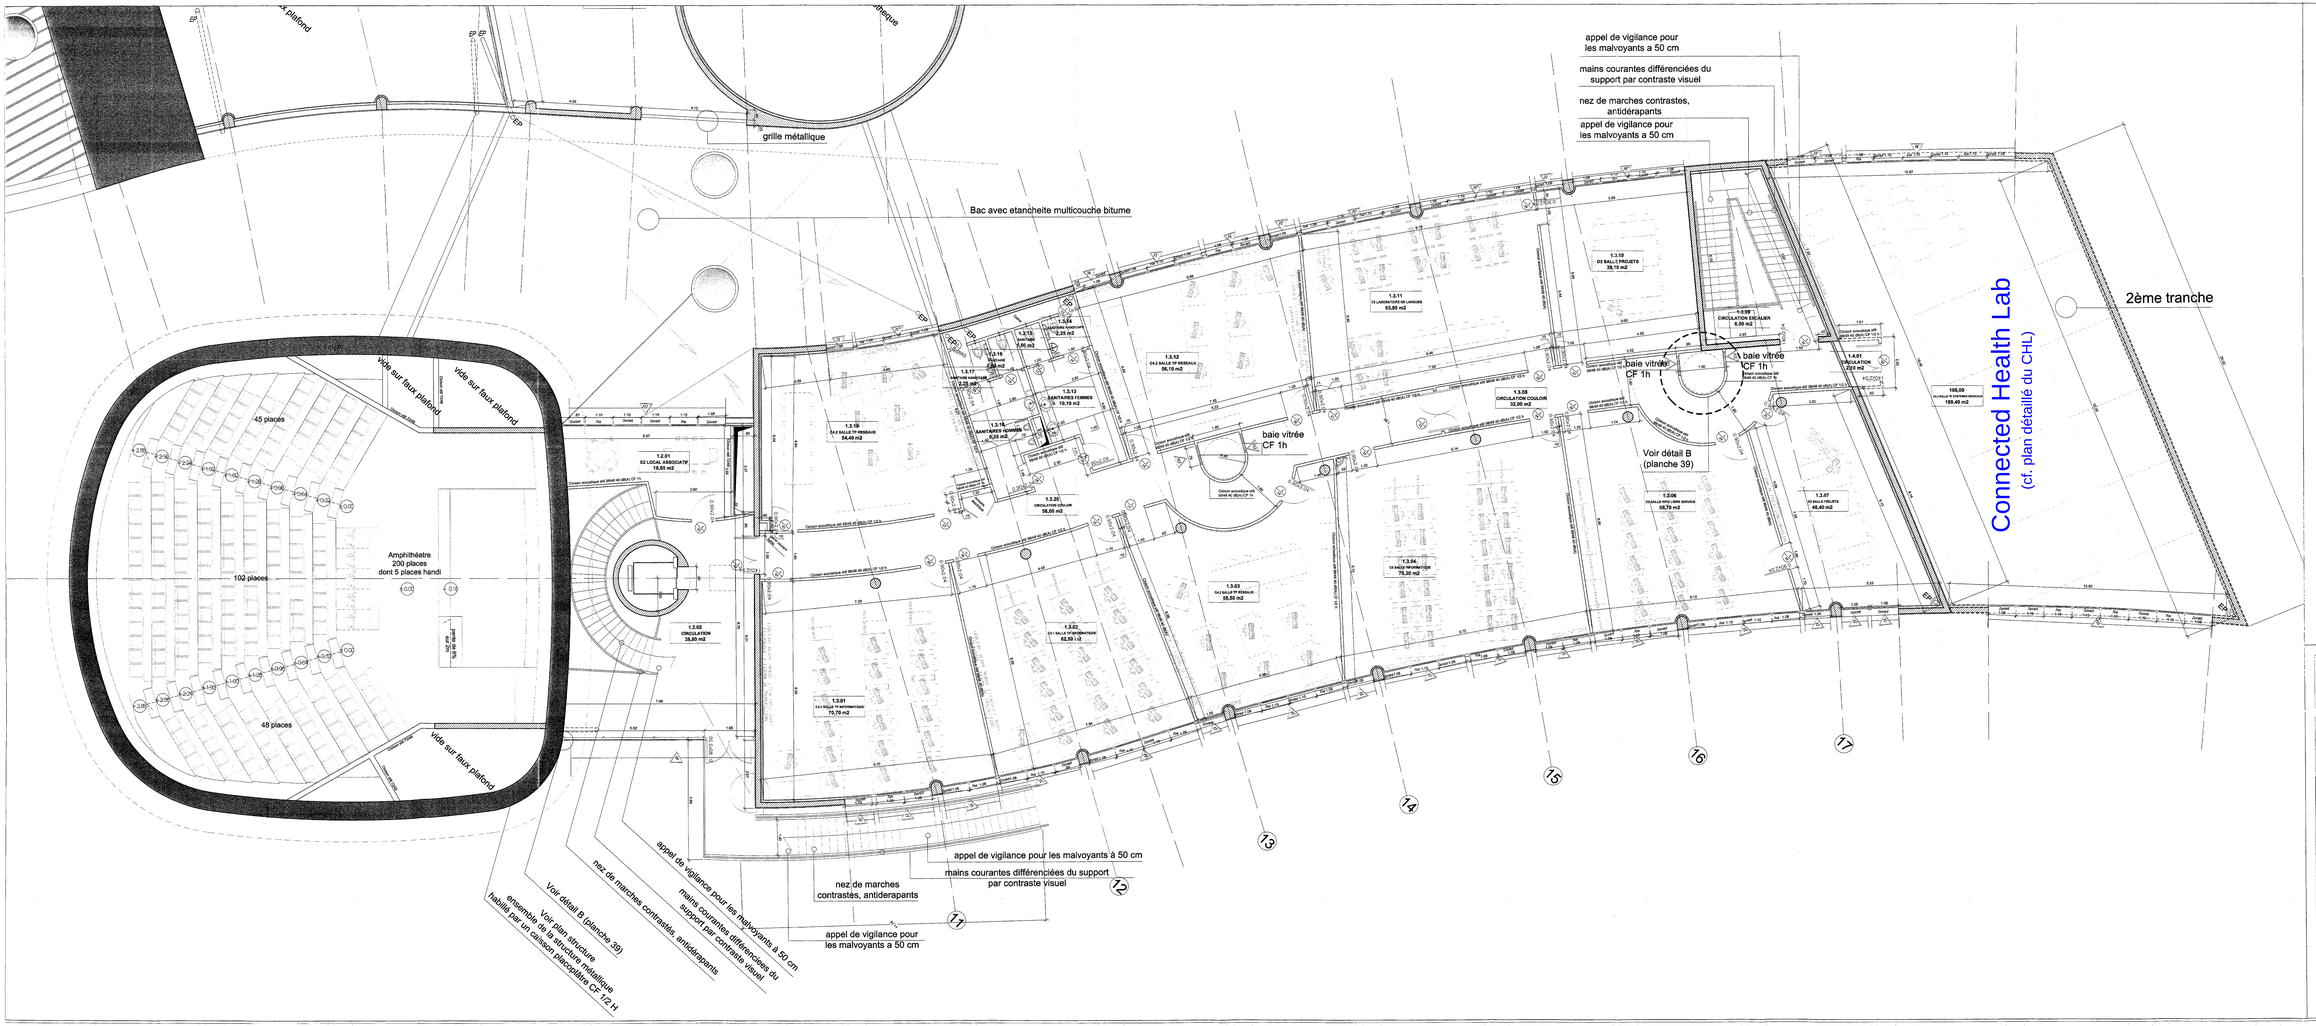

Mur en parpaing 200 mm

Cloison acoustique still 98/48 40 dB(A) CF 1h

Cloison acoustique still 98/48 40 dB(A) CF 1/2 h

Cloison acoustique still 98/48 40 dB(A)

Cloison still 72/48

Béton armé

MAITRE D'OUVRAGE :

LE SYNDICAT MIXTE pour le DEVELOPPEMENT de L'ENSEIGNEMENT SUPERIEUR, de la RECHERCHE et du TRANSFERT DE TECHNOLOGIE du SUD du TARN
Avenue Georges POMPIDOU
BP 258 - 81100 CASTRES CEDEX
Tel : 05.63.62.81.44

MAITRE D'OUVRAGE DELEGUE

SEM 81
LE CHOISE - Espace d'Entreprise
27-115 CASTRES
Tel : 05.63.72.42.42
Fax : 05.63.72.42.47

Formation d'ingénieurs ISIS

Commune de Castres - Lieu-dit "L'Espinasse" - Rue Firmin Oules
CASTRES

PLAN R+1 (1)

MANDATAIRE
ARCHITECTE

ROGER TAILLIBERT
ARCHITECTE DE L'ART S.E.A.R.L
153 RUE DE LA POMPE
75016 PARIS
TEL : 33 47 04 29 62
FAX : 33 47 27 27 75
E-mail : rtaillibert-r@dial.oleane.com

B.E.C.

SERGE BUREAU D'ETUDES TECHNIQUES
ZTS CENTRE COMMERCIAL DIVORCE - Avenue de Lardenne
31084 TOULOUSE
TEL : 05.61.73.64.00 FAX : 05.61.73.16.03

VERITAS BUREAU DE CONTROLE
Zone commerciale de Lescuyer - Lieu dit Lampajoye
81100 LESCUYER CPALIE
TEL : 05.63.70.17.04 FAX : 05.63.70.40.51

SOGABE ETS
Rue Firmin Oules - Le Tillou
81100 CASTRES
TEL : 05.63.51.04.95

DOSSIER DE CONSULTATION DES ENTREPRISES

N° ART : 27.00 DATE : 22-JUILLET-2008 ECHELLE : 1/50

INDICE	MODIFICATIONS DU DOCUMENT	ETABLI PAR	VERIFIE PAR	DATE
A	Ajout des sous 4" NEIRIERS			AOUT 2008
B	Mises tout chaufferie			SEPT. 2008

PERMIS DE CONSTRUIRE N° DU DATE DU

PHASE	ENSTRUA	TYPE	ZONE	NIVEAU	LOT	DOMAINE	NUMERO	INDICE
DCE	-						ISIS-11A	B